



Arquitectura · 5è curs

Nicolau Camprubí Pijuan

Barcelona
+34 629 054 477
nicocamprubi@gmail.com

experiència teòrica

Grau superior · Universitat Politècnica de Catalunya, ETSAV

Intercanvi · Lucerne University of Applied Sciences and Arts, HSLU

MH · Geometria Analítica, Composició III, Taller d'Arquitectura i Projectes V

experiència pràctica

8h Studio 2026

Pratiques extracurriculares · Aprenent de retail

- Aplicació d'estandards de marca
- Desenvolupament d'avantprojectes i executius

Jornet Llop Pastor Arquitectes 2025

Pratiques curriculares · Aprenent d'urbanisme

- Cartografia, mapes i treball amb GIS
- Suport a projectes i documentació tècnica
- Estudis urbanístics i redacció de normativa

Other Structures 2024

Pratiques extracurriculares · Aprenent d'estructures

- Treball amb metodologia BIM i modelització estructural
- Dibuix, càlculs bàsics i documentació tècnica
- Automatització de processos i coordinació amb arquitectura

Voluntariat (Alemanya) 2023

Construcció d'un model d'habitabilitat sostenible

Altres experiències 2020–2023

Atenció infantil · Personal de sala · Cambrer · Assistent de magatzem

programari

Altes competències

AutoCAD · Microstation · Photoshop · DaVinci Resolve

Nocions

InDesign · Revit · Metodologia BIM · GIS · Dialux

idiomes


Altes competències

Català · Castellà · Anglès

Penombra

Enunciat Projectes V · Redefinir l'habitabilitat de manera normal-radical
L'arquitectura es projecta per convocar la llum: un fenomen incontrolable que dota l'espai d'una dimensió emocional. La seva justa presència permet que, al ritme dels cicles solars, els rituals quotidians transitin entre la claror i la penombra.




Aquesta voluntat expressiva es materialitza a través d'una pell estructural que actua com a regulador climàtic. El sistema integra murs Trombe per a la captació tèrmica, l'efecte stack per a la ventilació natural i una orientació estratègica de les obertures. El conjunt combina la inèrcia interior amb un aïllament tèrmic eficient, garantint el confort passiu sense renunciar a la poètica de l'espai habitat.

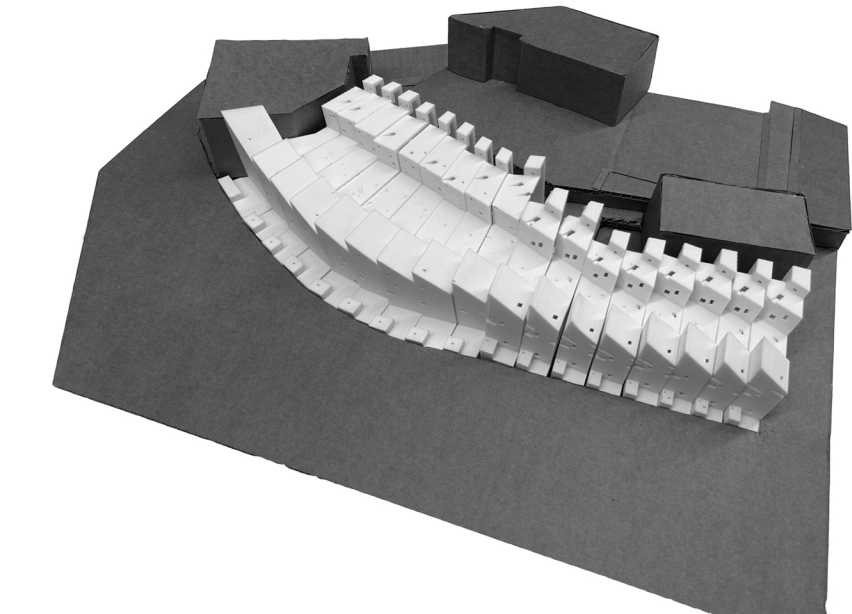


maqueta emplaçament




espai emocional · foto maqueta 1:20

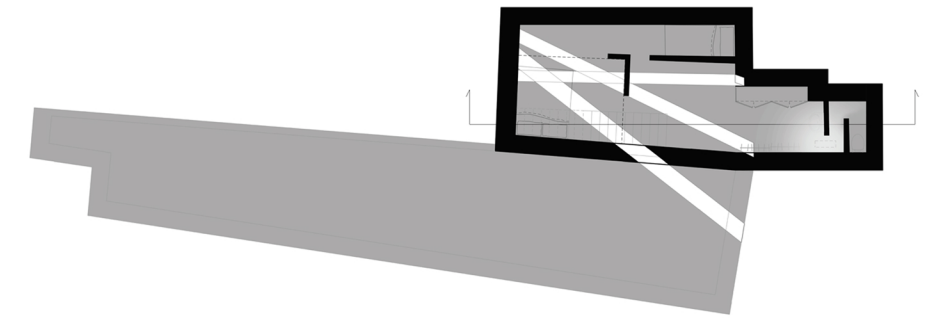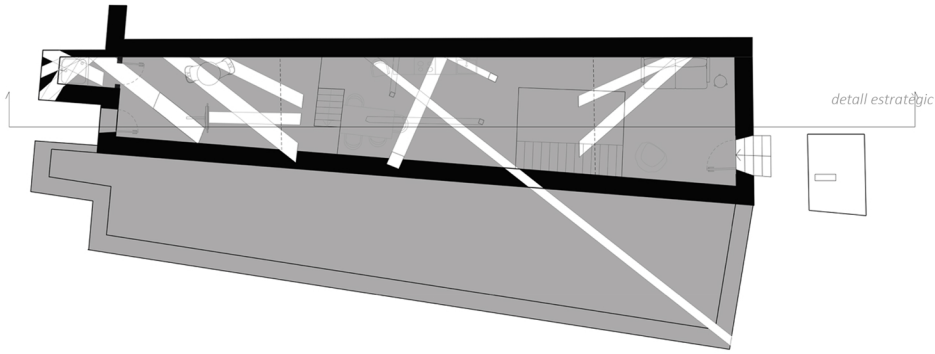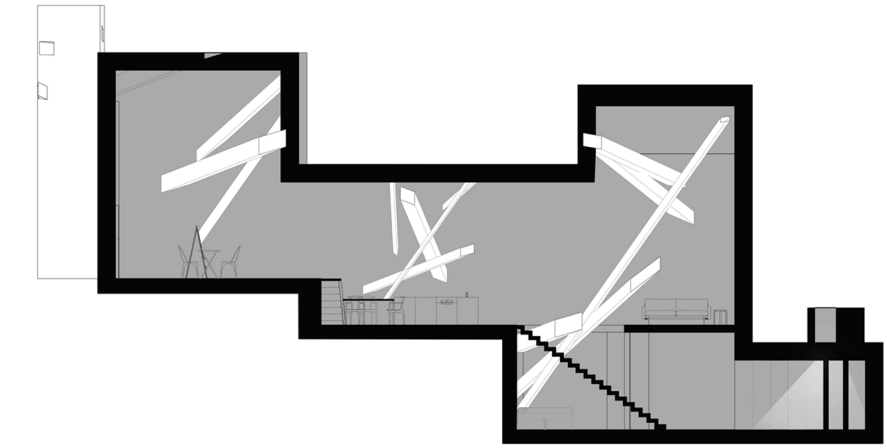


anàlisi del sumatori de projeccions lumíniques naturals

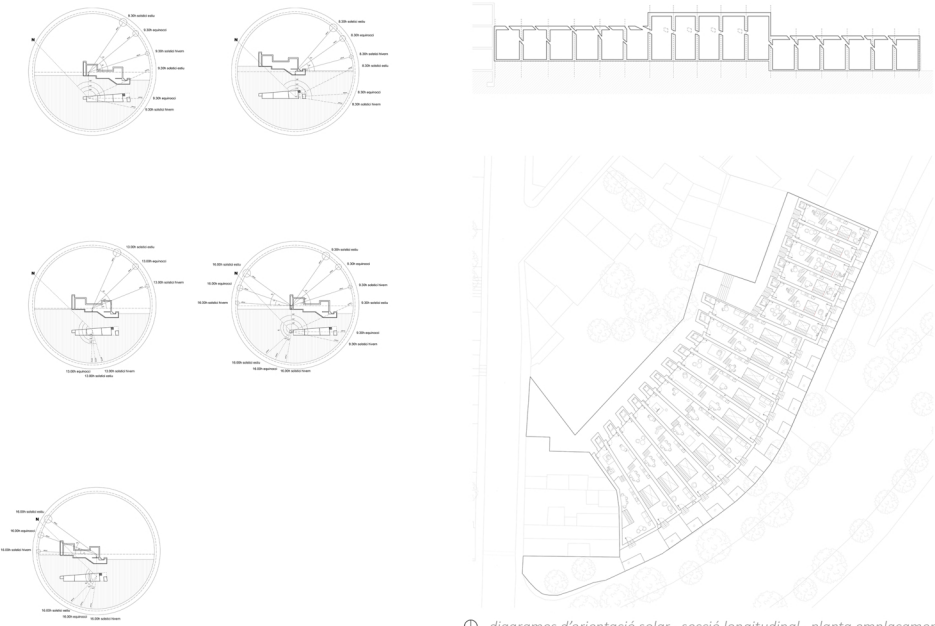

diagrames d'orientació solar · secció longitudinal · planta emplaçament

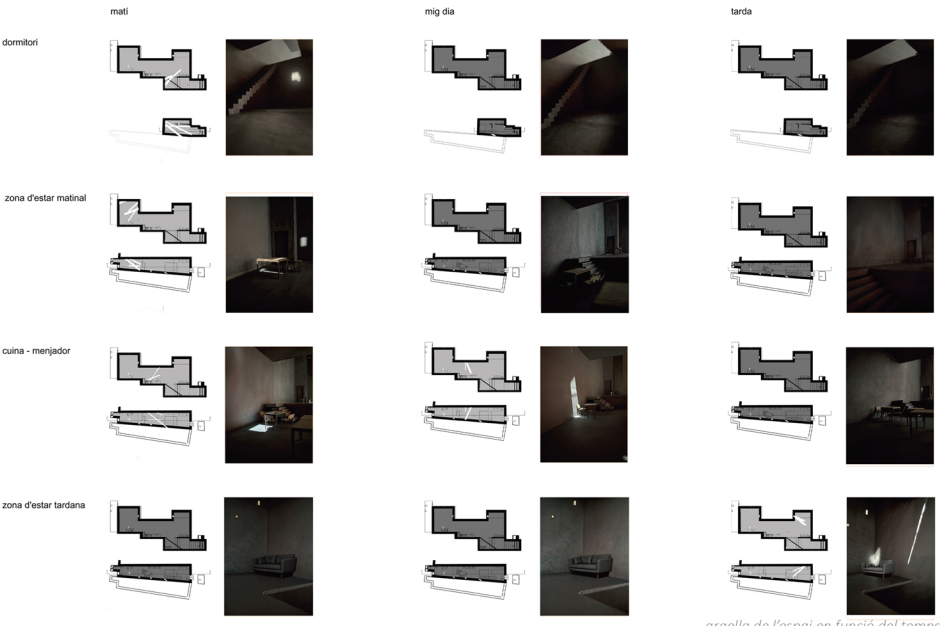

graella de l'espai en funció del temps

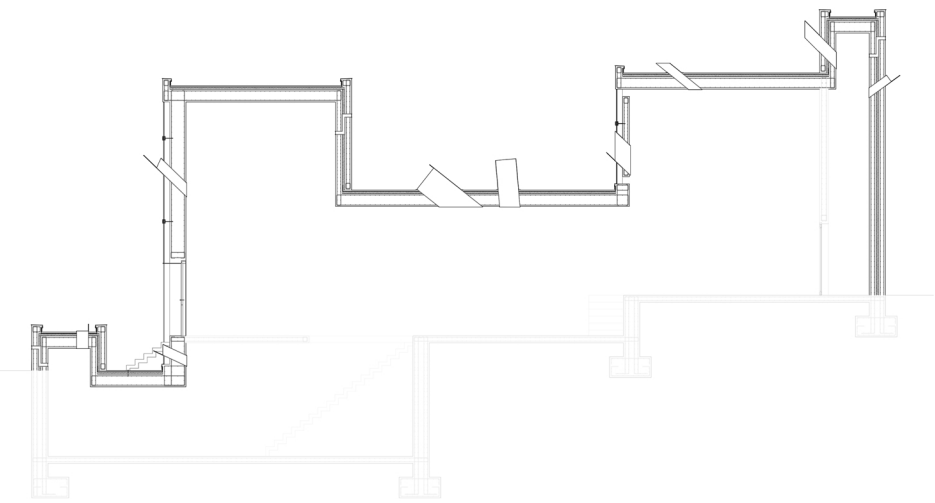

detall estratègic

Simbiosis Climàtiques


Enunciat Projectes X · Intervenció oberta en l'entorn consolidat del Raval

L'efecte illa de calor, la pobresa energètica i l'obsolescència del parc residencial accentuen la vulnerabilitat del Raval Nord. Davant d'aquest escenari, el projecte proposa una xarxa de refugis climàtics cohesionada i replicable que neix d'una anàlisi crítica de les infraestructures actuals.


La intervenció no ocupa espais residuals, sinó que activa l'interstici entre equipaments i espai públic. Mitjançant un sistema constructiu únic i adaptable, els retranquejos i la mateixa trava estructural generen àmbits apropiables que garanteixen el confort tèrmic. El resultat és una arquitectura que reforça la continuïtat i la relació activa entre l'equipament i l'espai públic.






diàleg amb les preexistències · collages

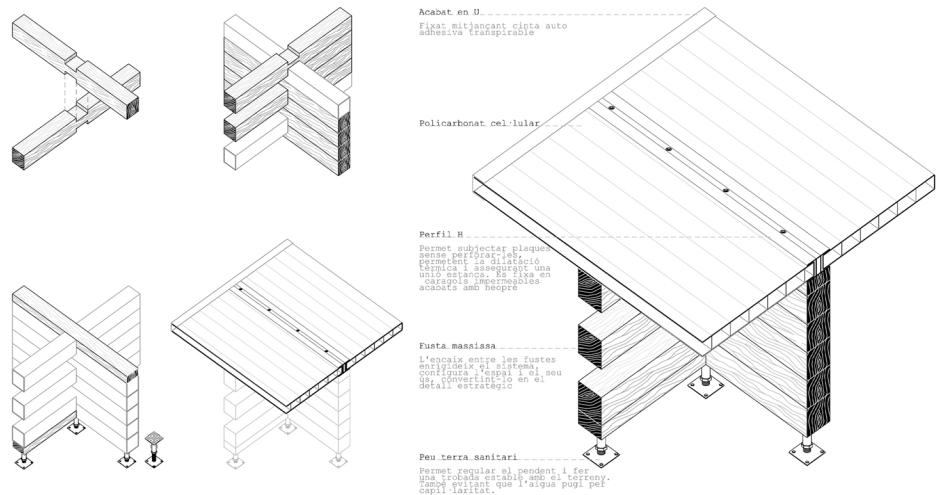


detall estratègic

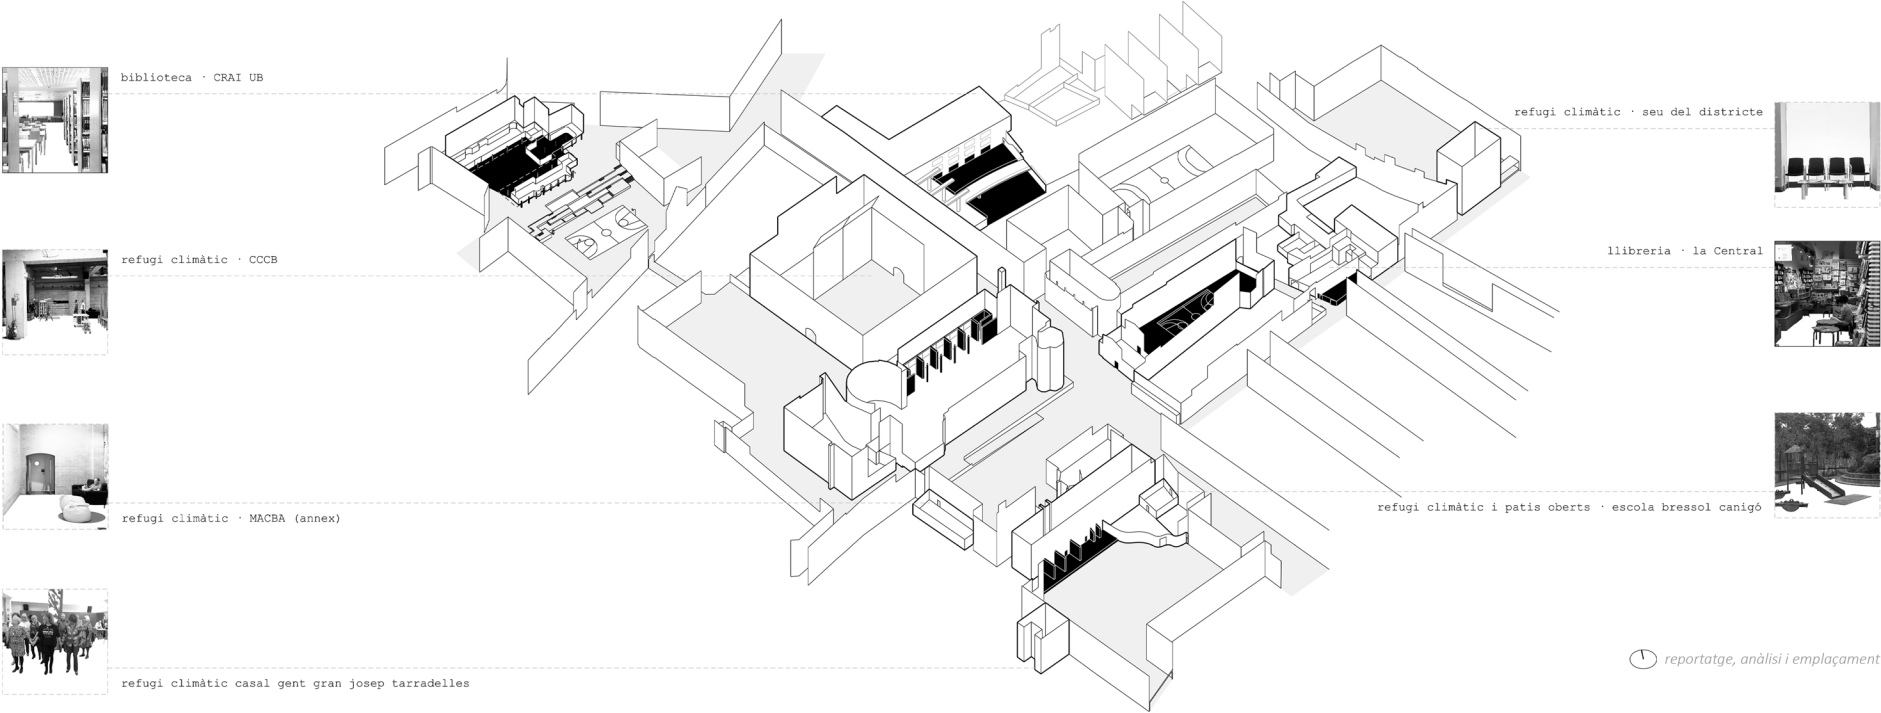


reportatge, anàlisi i emplaçament

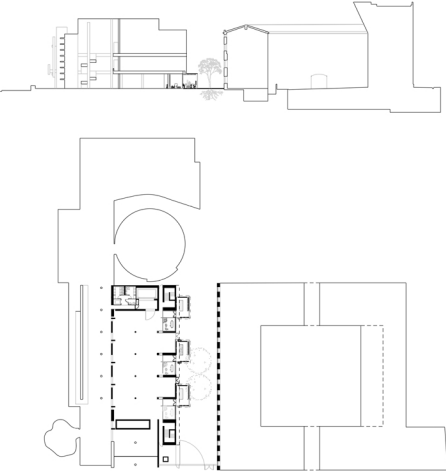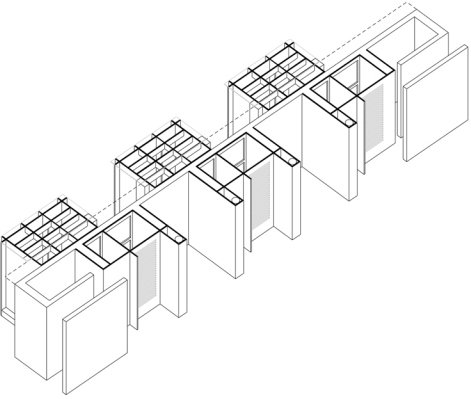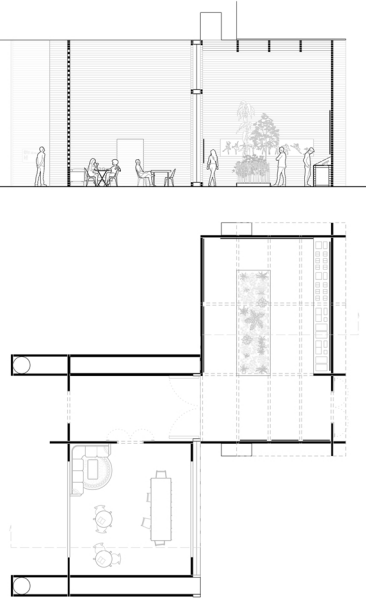

plantas i seccions peça · intervenció MACBA · plantas i seccions contextuais

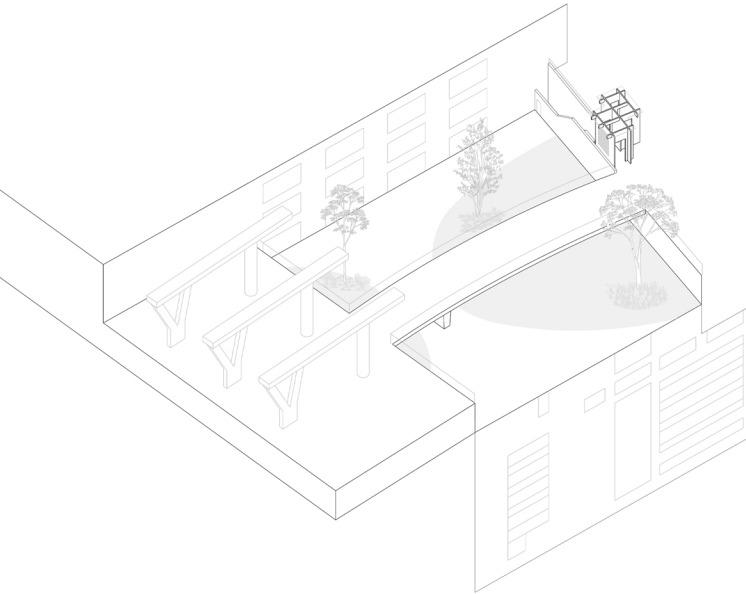

intervenció biblioteca CRAI

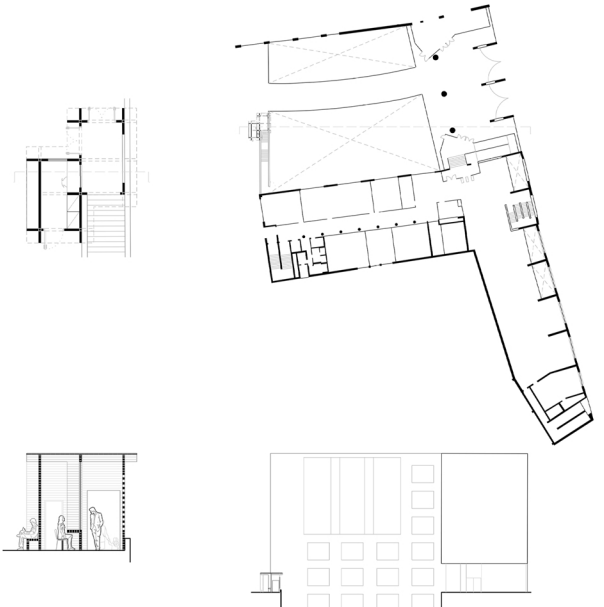

plantas i seccions peça · plantas i seccions contextuais

Grossform

Enunciat Spekulation Arkitektur · Utilitzar la Grossform en un entorn suburbial
Ebikon, a Suïssa, es configura com un àmbit lineal i fragmentat, condicionat per la topografia i les grans infraestructures entre Lucerna i Zúric. Aquesta situació ha generat un espai residual entre la via del tren i el riu, ocupat per peces autònomes desvinculades de la centralitat urbana. Davant d'aquesta desarticulació, el concepte de Grossform “Coherència formal” permet posar en valor la riquesa heterogènia del lloc i unificar-lo com un conjunt, oscil·lant entre l'escala urbanística i l'arquitectònica.


La intervenció activa el valor latent mitjançant una geometria contínua que integra els elements existents i cus la seqüència d'espais des de l'àrea industrial fins al llac. Aquesta acció és només l'inici, perquè el vertader interès recau en com reacciona al seu entorn.




espai emocional estació de tren · foto maqueta 1:50




espai polivalent · foto maqueta 1:50

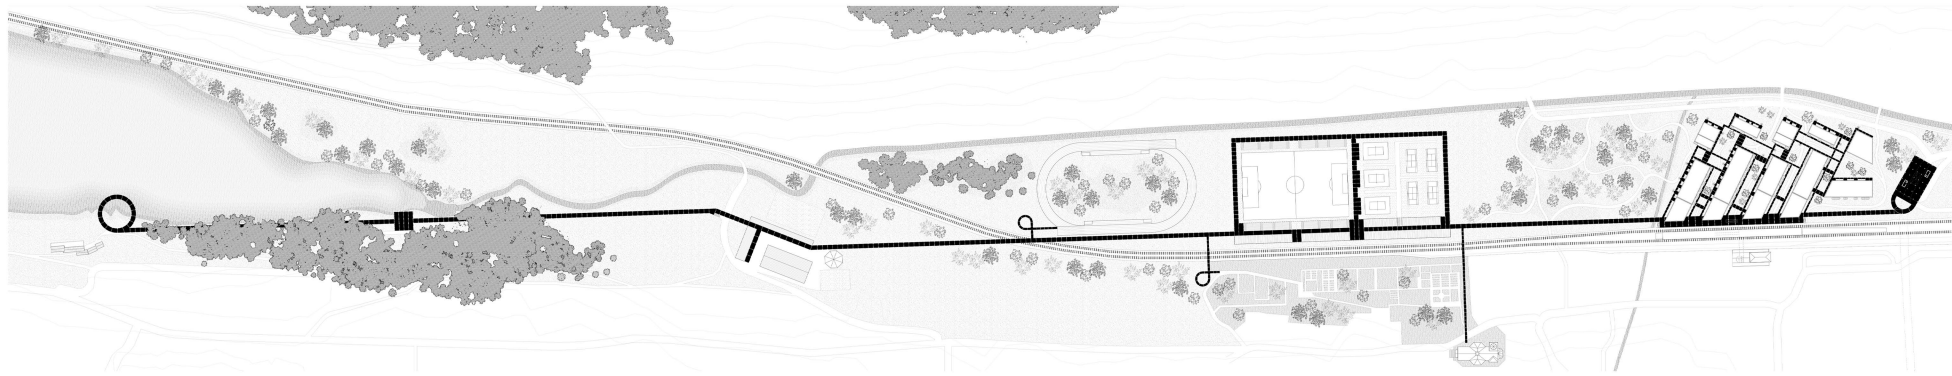

mapa territorial

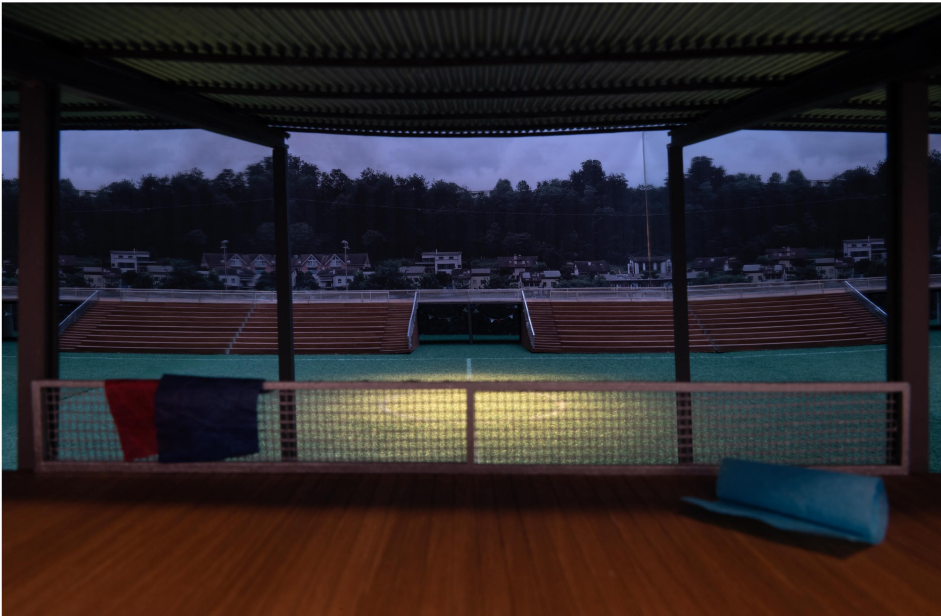

complex esportiu · foto maqueta 1:50

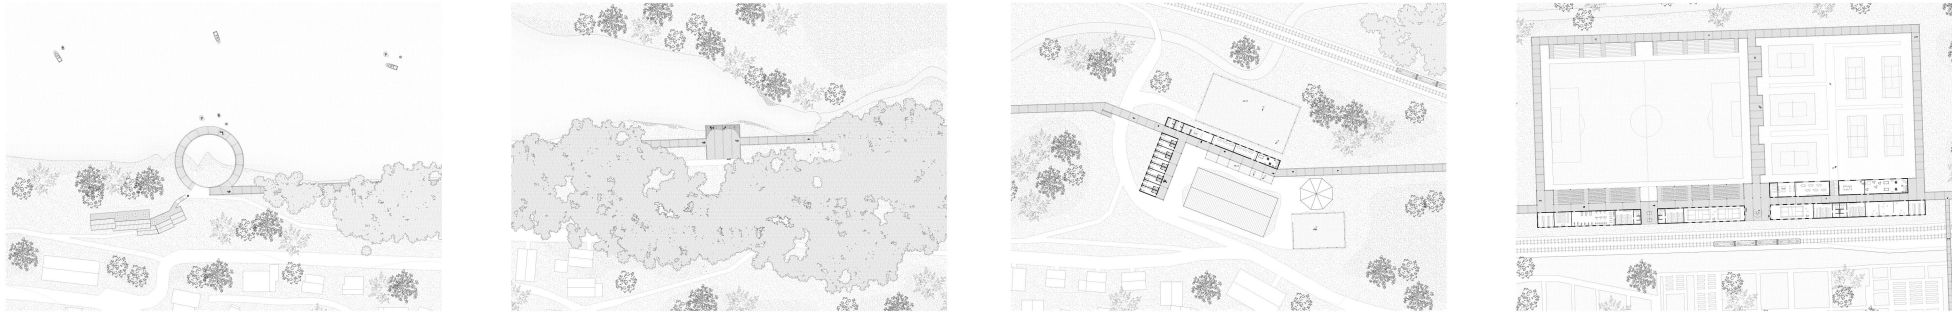

llac · bosc

granja · complex esportiu



complex residencial · pas de cotxes soterrat i garatge

Igualació

Enunciada Intervenció · Com intervenir en el parc edificat Cal Paua, masia situada a Meranges, Cerdanya. Es rehabilita per adaptar-se als nous usos socioculturals després d'anys d'abandonament. La intervenció posa en valor la preexistència mitjançant un programa d'accions que garanteix el compliment normatiu i prioritza el confort passiu.

- Les estratègies són, buidatge dels tres volums nobles i utilitza un sistema box-in-box a les zones perimetrals per donar continuïtat al conjunt. Es defineixen així dos llenguatges.
- Preexistència, inèrcia, col·lectivitat
 - Afegit, lleugeresa, individual

